



LANDSCAPE AREA SALERNO RANCH

NOTE C.C.R. SECTION 4.9 MAINTENANCE LAWNS/PLANTINGS TREES BETWEEN FRONT OF LOT TO PAVING ARE RESPONSIBILITY OF LOT OWNER AS TO TRIMMING AND GENERAL APPEARANCE

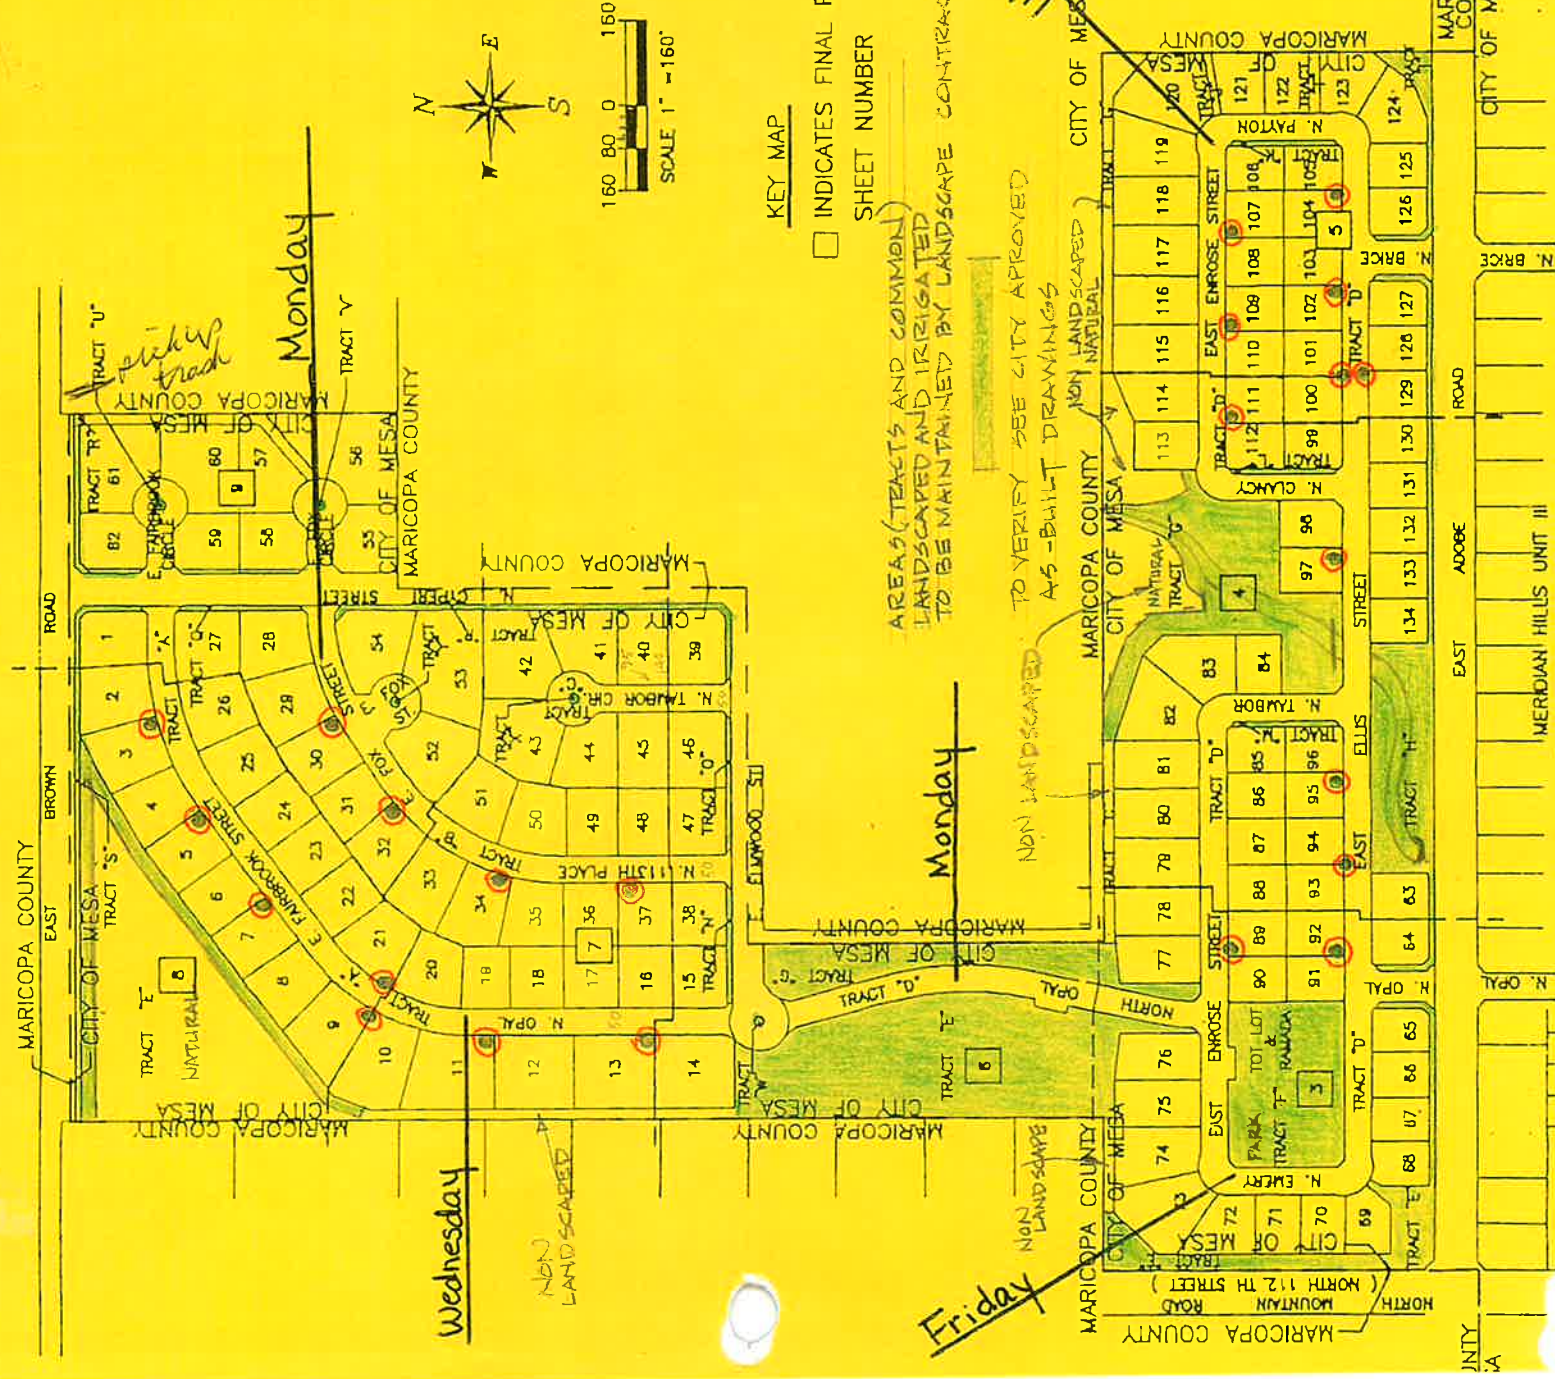

Salerno Ranch

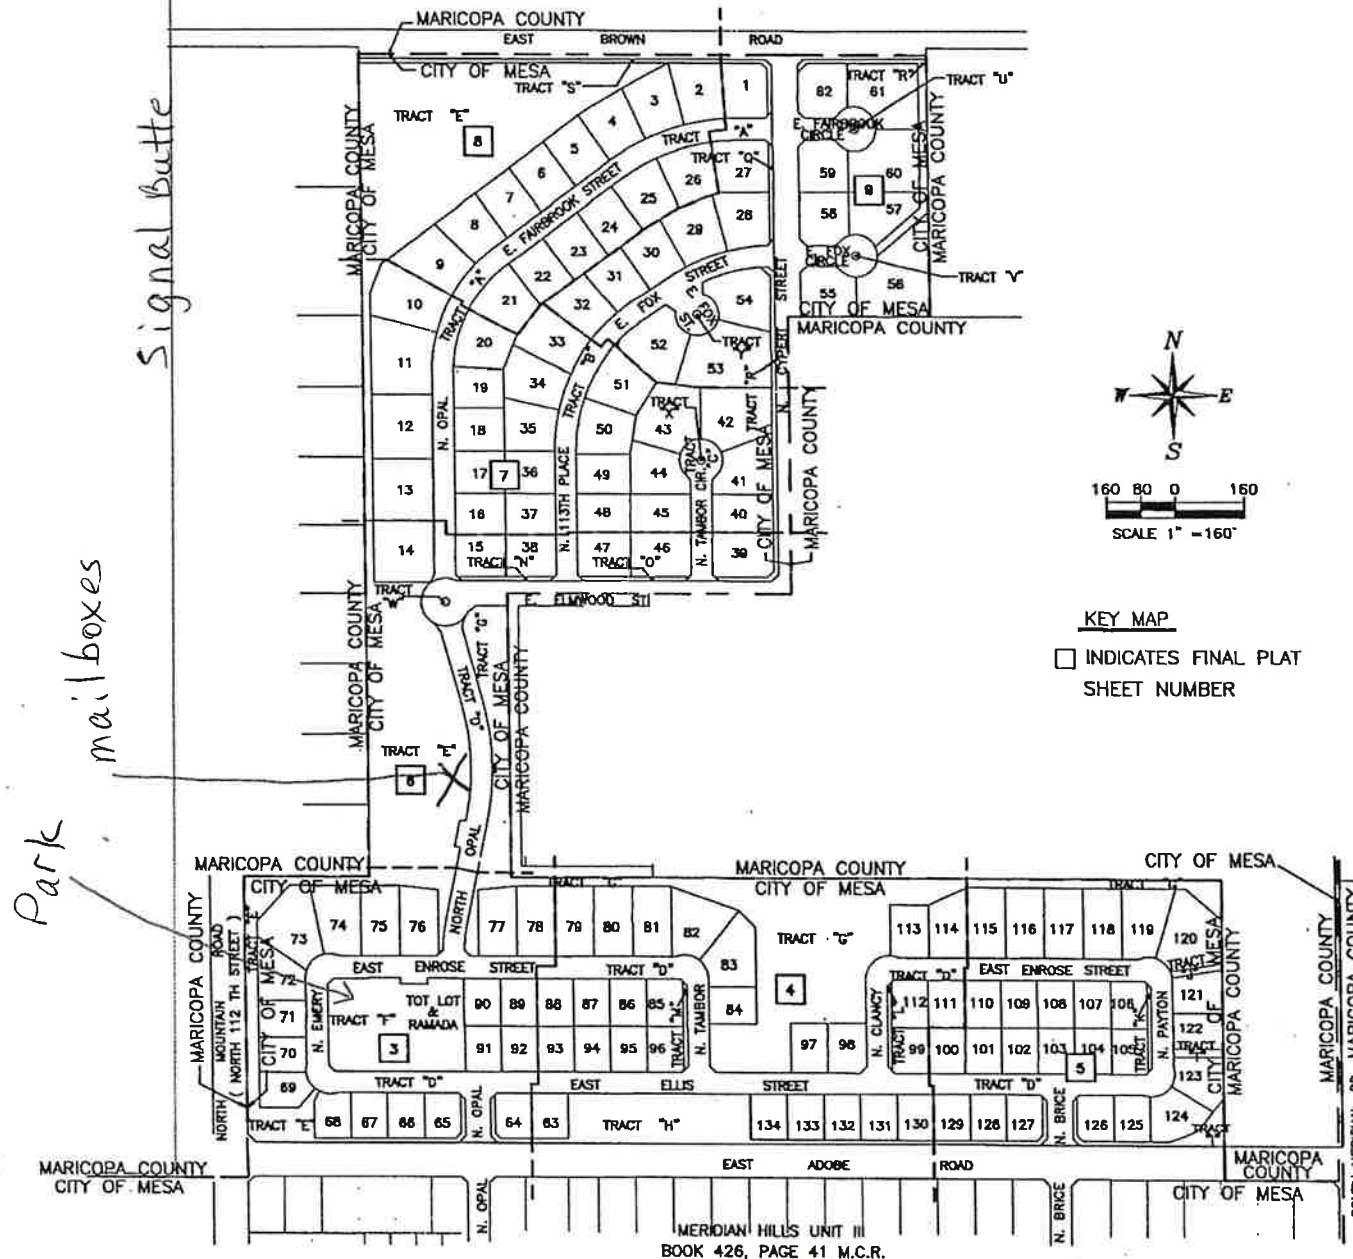


LOT AREAS		
LOT	AREA	
1	12,765 SQ. FT.	0.2930 ACRES
2	14,581 SQ. FT.	0.3347 ACRES
3	14,591 SQ. FT.	0.3350 ACRES
4	13,402 SQ. FT.	0.3077 ACRES
5	12,611 SQ. FT.	0.2883 ACRES
6	12,500 SQ. FT.	0.2870 ACRES
7	12,500 SQ. FT.	0.2870 ACRES
8	13,603 SQ. FT.	0.3123 ACRES
9	17,030 SQ. FT.	0.3905 ACRES
10	20,703 SQ. FT.	0.4735 ACRES
11	23,728 SQ. FT.	0.5447 ACRES
12	21,000 SQ. FT.	0.4821 ACRES
13	21,000 SQ. FT.	0.4821 ACRES
14	20,554 SQ. FT.	0.4704 ACRES
15	11,938 SQ. FT.	0.2738 ACRES
16	11,833 SQ. FT.	0.2716 ACRES
17	11,833 SQ. FT.	0.2716 ACRES
18	11,833 SQ. FT.	0.2716 ACRES
19	10,913 SQ. FT.	0.2505 ACRES
20	14,222 SQ. FT.	0.3265 ACRES
21	15,052 SQ. FT.	0.3455 ACRES
22	12,798 SQ. FT.	0.2933 ACRES
23	12,296 SQ. FT.	0.2823 ACRES
24	12,296 SQ. FT.	0.2823 ACRES
25	13,934 SQ. FT.	0.3199 ACRES
26	14,141 SQ. FT.	0.3248 ACRES
27	14,928 SQ. FT.	0.3427 ACRES
28	14,474 SQ. FT.	0.3323 ACRES
29	15,434 SQ. FT.	0.3543 ACRES
30	13,098 SQ. FT.	0.3007 ACRES
31	12,073 SQ. FT.	0.2772 ACRES
32	13,485 SQ. FT.	0.3096 ACRES
33	15,668 SQ. FT.	0.3597 ACRES
34	15,373 SQ. FT.	0.3529 ACRES
35	13,579 SQ. FT.	0.3117 ACRES
36	11,847 SQ. FT.	0.2720 ACRES
37	11,874 SQ. FT.	0.2718 ACRES
38	11,840 SQ. FT.	0.2741 ACRES
39	15,047 SQ. FT.	0.3454 ACRES
40	13,352 SQ. FT.	0.3065 ACRES
41	15,226 SQ. FT.	0.3492 ACRES
42	20,903 SQ. FT.	0.4799 ACRES
43	18,754 SQ. FT.	0.4305 ACRES
44	13,800 SQ. FT.	0.3148 ACRES
45	13,300 SQ. FT.	0.3053 ACRES
46	15,095 SQ. FT.	0.3465 ACRES
47	13,478 SQ. FT.	0.3094 ACRES
48	11,875 SQ. FT.	0.2726 ACRES
49	11,875 SQ. FT.	0.2726 ACRES
50	14,311 SQ. FT.	0.3331 ACRES
51	15,250 SQ. FT.	0.3501 ACRES
52	18,606 SQ. FT.	0.4271 ACRES
53	27,821 SQ. FT.	0.6387 ACRES
54	17,546 SQ. FT.	0.4018 ACRES
55	14,851 SQ. FT.	0.3363 ACRES
56	28,863 SQ. FT.	0.6628 ACRES
57	14,244 SQ. FT.	0.3270 ACRES
58	13,297 SQ. FT.	0.3043 ACRES
59	13,297 SQ. FT.	0.3043 ACRES
60	21,217 SQ. FT.	0.4871 ACRES
61	22,026 SQ. FT.	0.5056 ACRES
62	13,581 SQ. FT.	0.3120 ACRES
63	9,350 SQ. FT.	0.2146 ACRES
64	9,350 SQ. FT.	0.2146 ACRES
65	9,350 SQ. FT.	0.2146 ACRES
66	9,350 SQ. FT.	0.2146 ACRES
67	9,350 SQ. FT.	0.2146 ACRES

Stain


Signal Butte

Salerno Ranch

Brown Rd

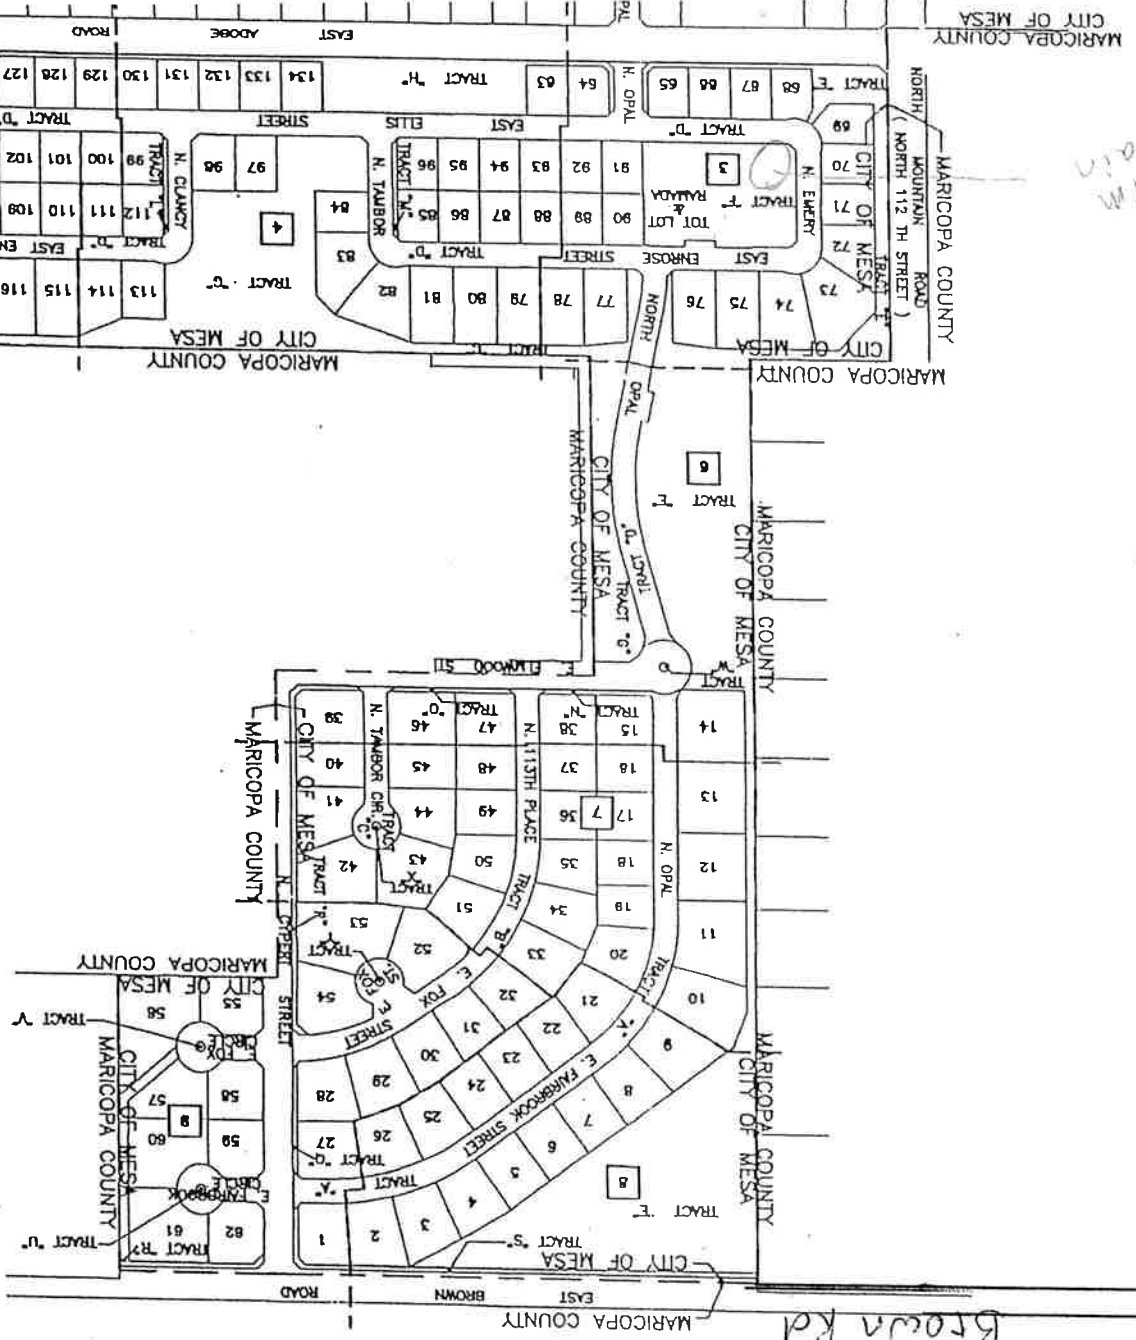


KEY MAP
☐ INDICATES FINAL PLAT
 SHEET NUMBER

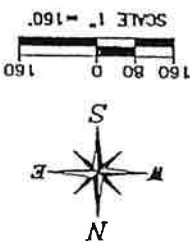


1	12.7
2	12.8
3	12.9
200	32.6

Salerno Ranch

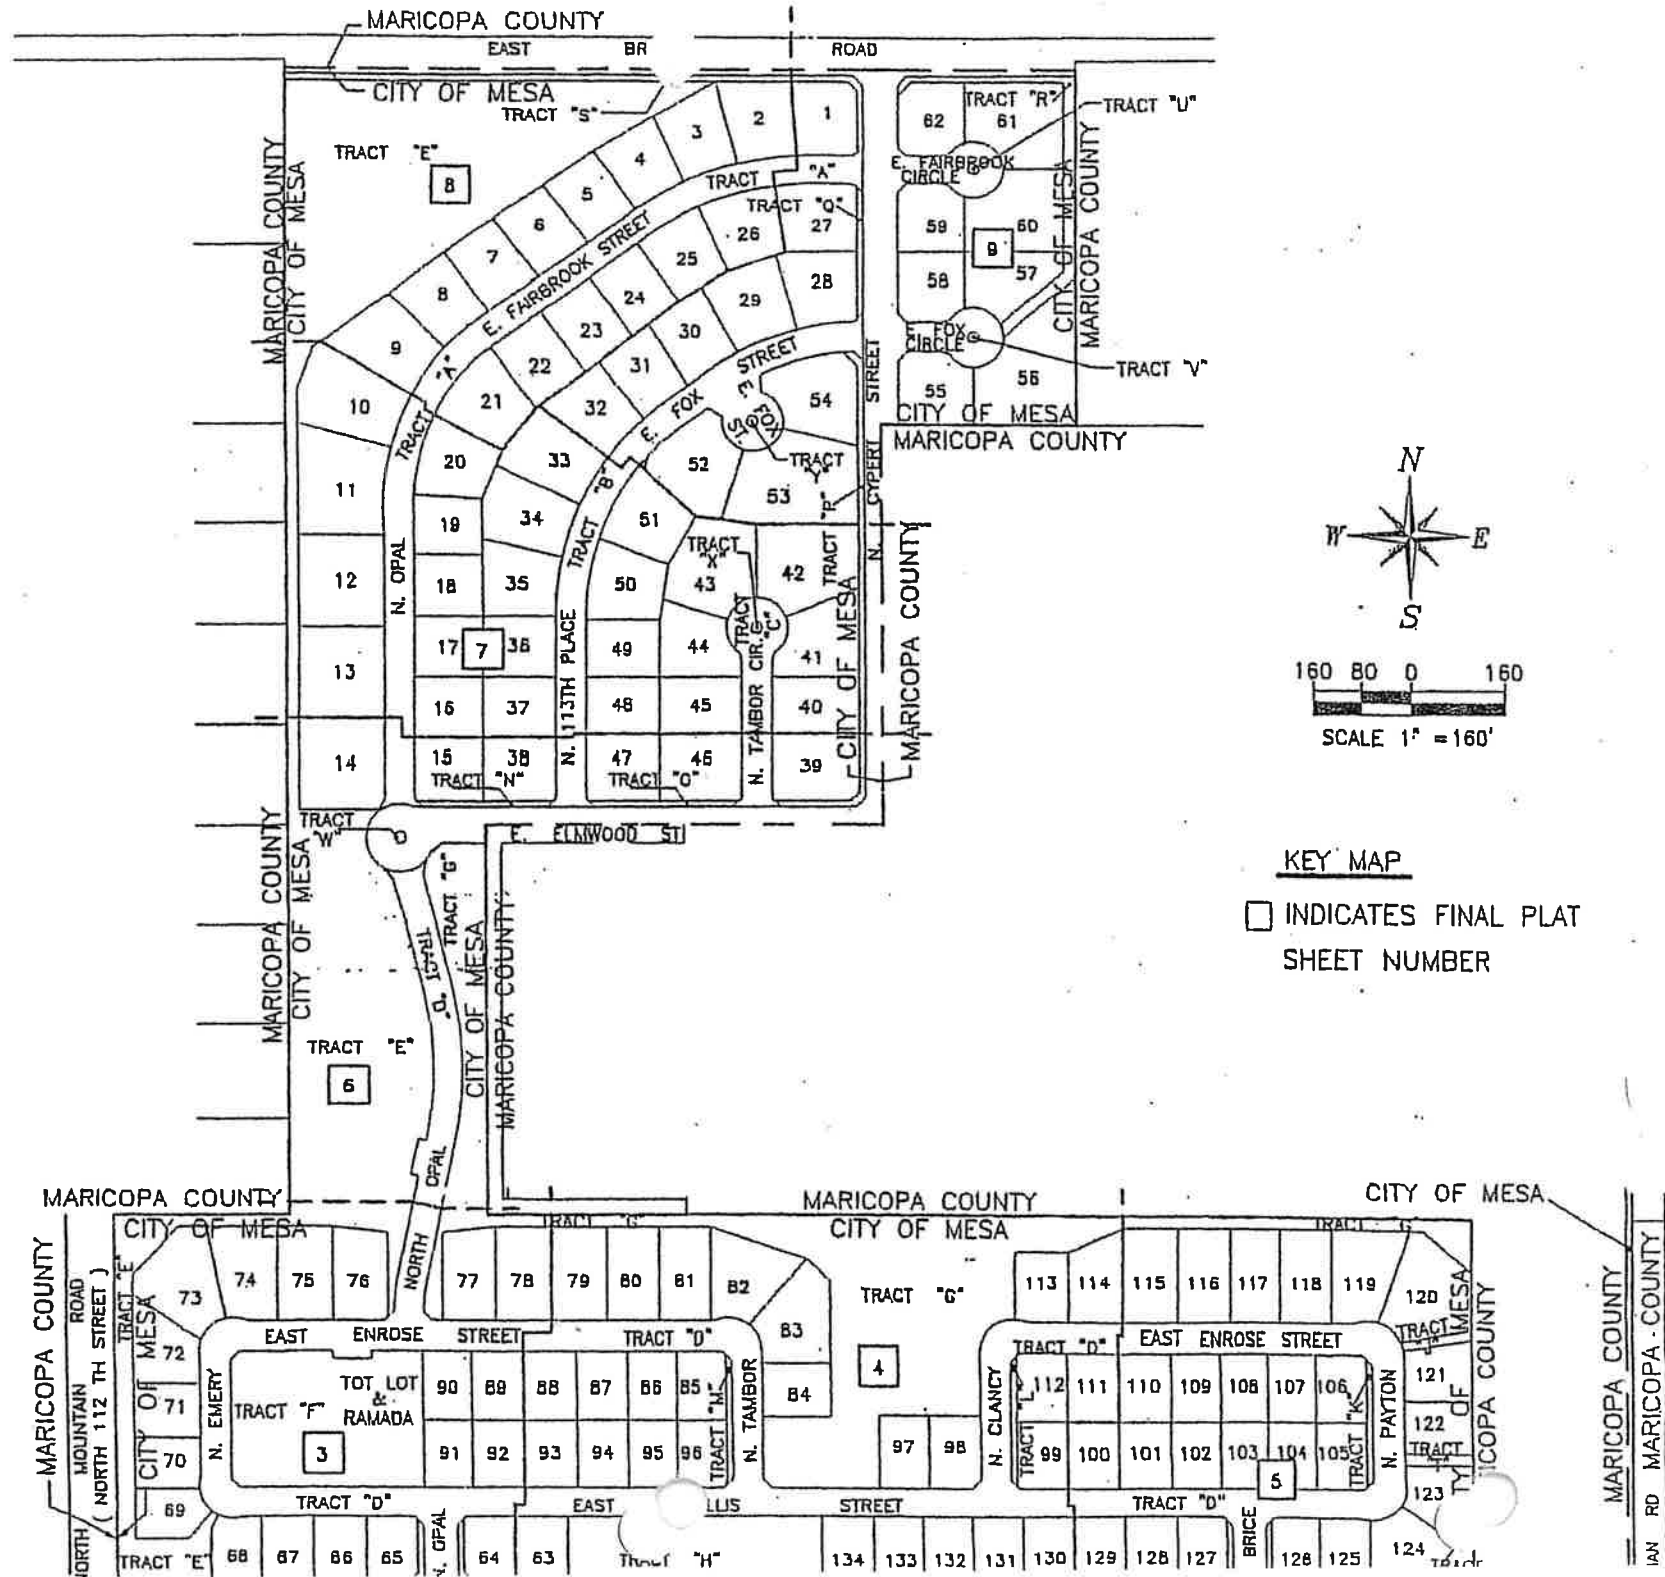


Salerino Ranch

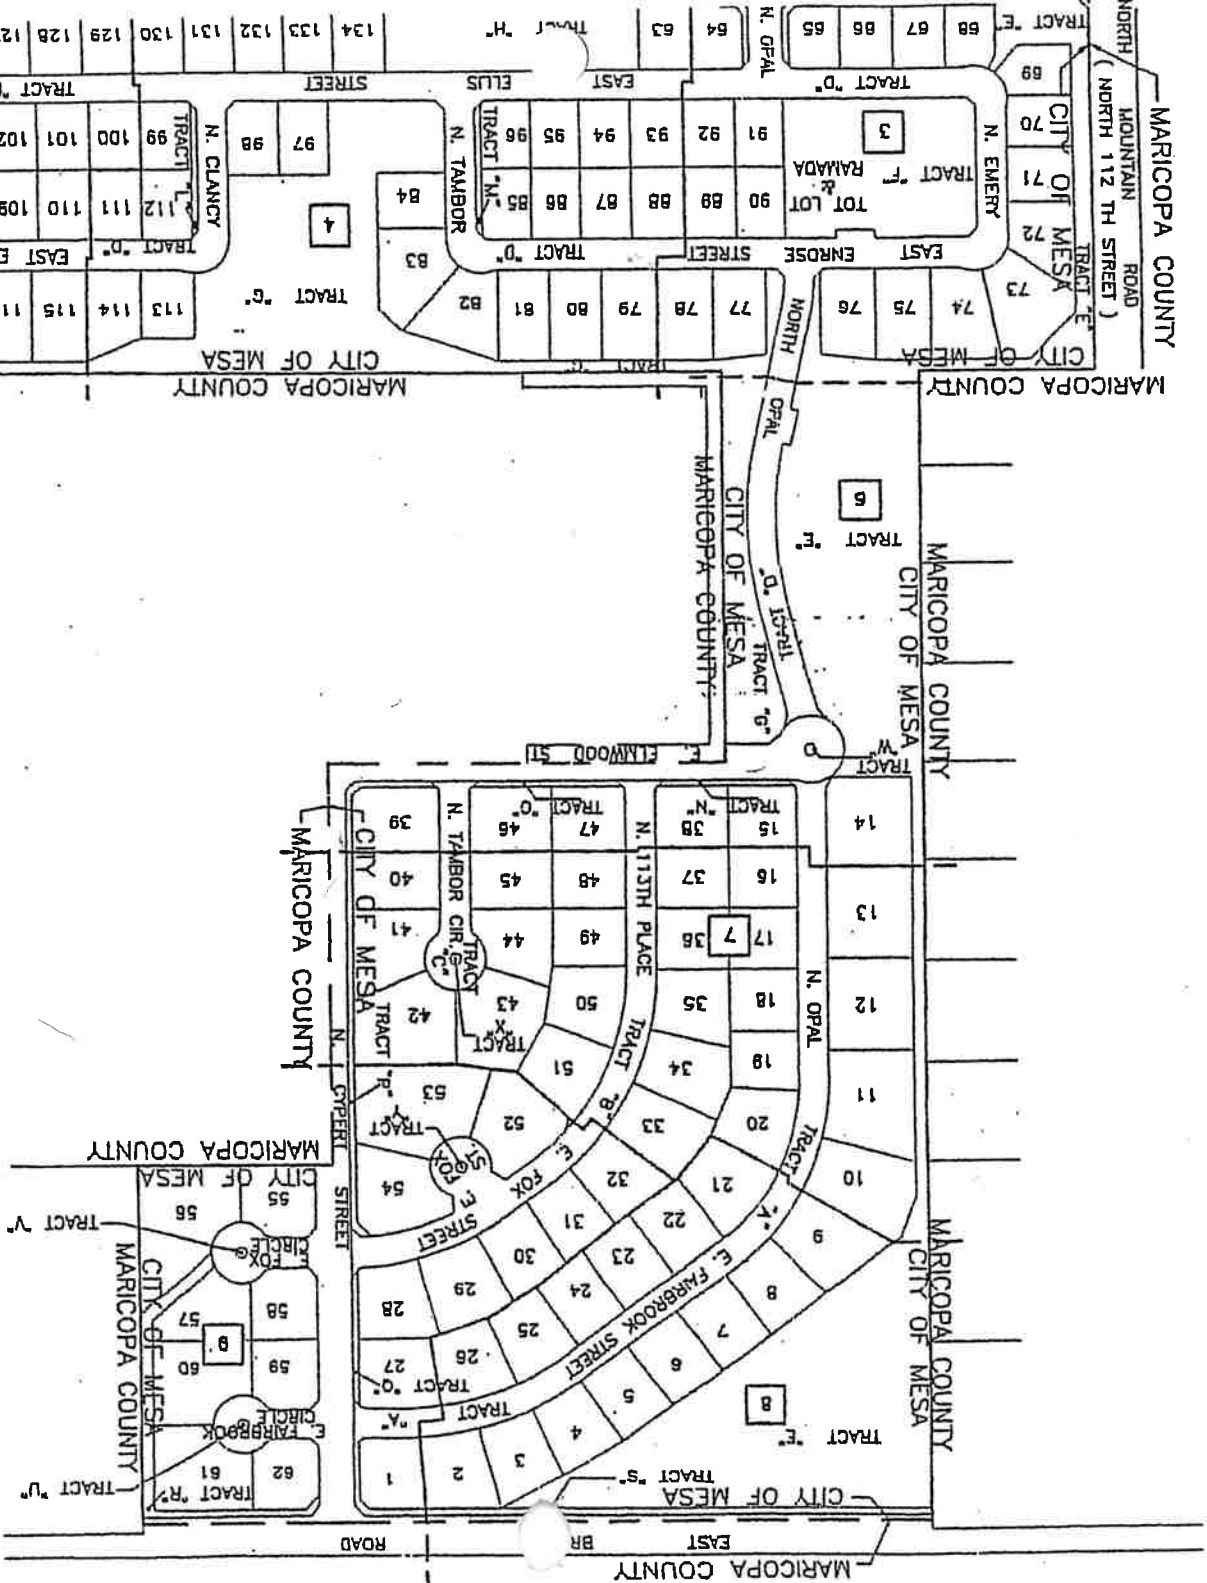


KEY MAP

☐ INDICATES FINAL PLAT
SHEET NUMBER

SCALE 1" = 160'

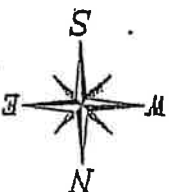

MARICOPA COUNTY
N RD MARICOPA COUNTY

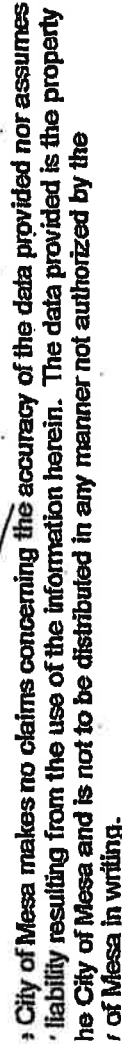


prepared on August 22, 2006 by the Neighborhood Outreach Office.



Great Danube Ninlilu. Confirmed

Salerno Ranch

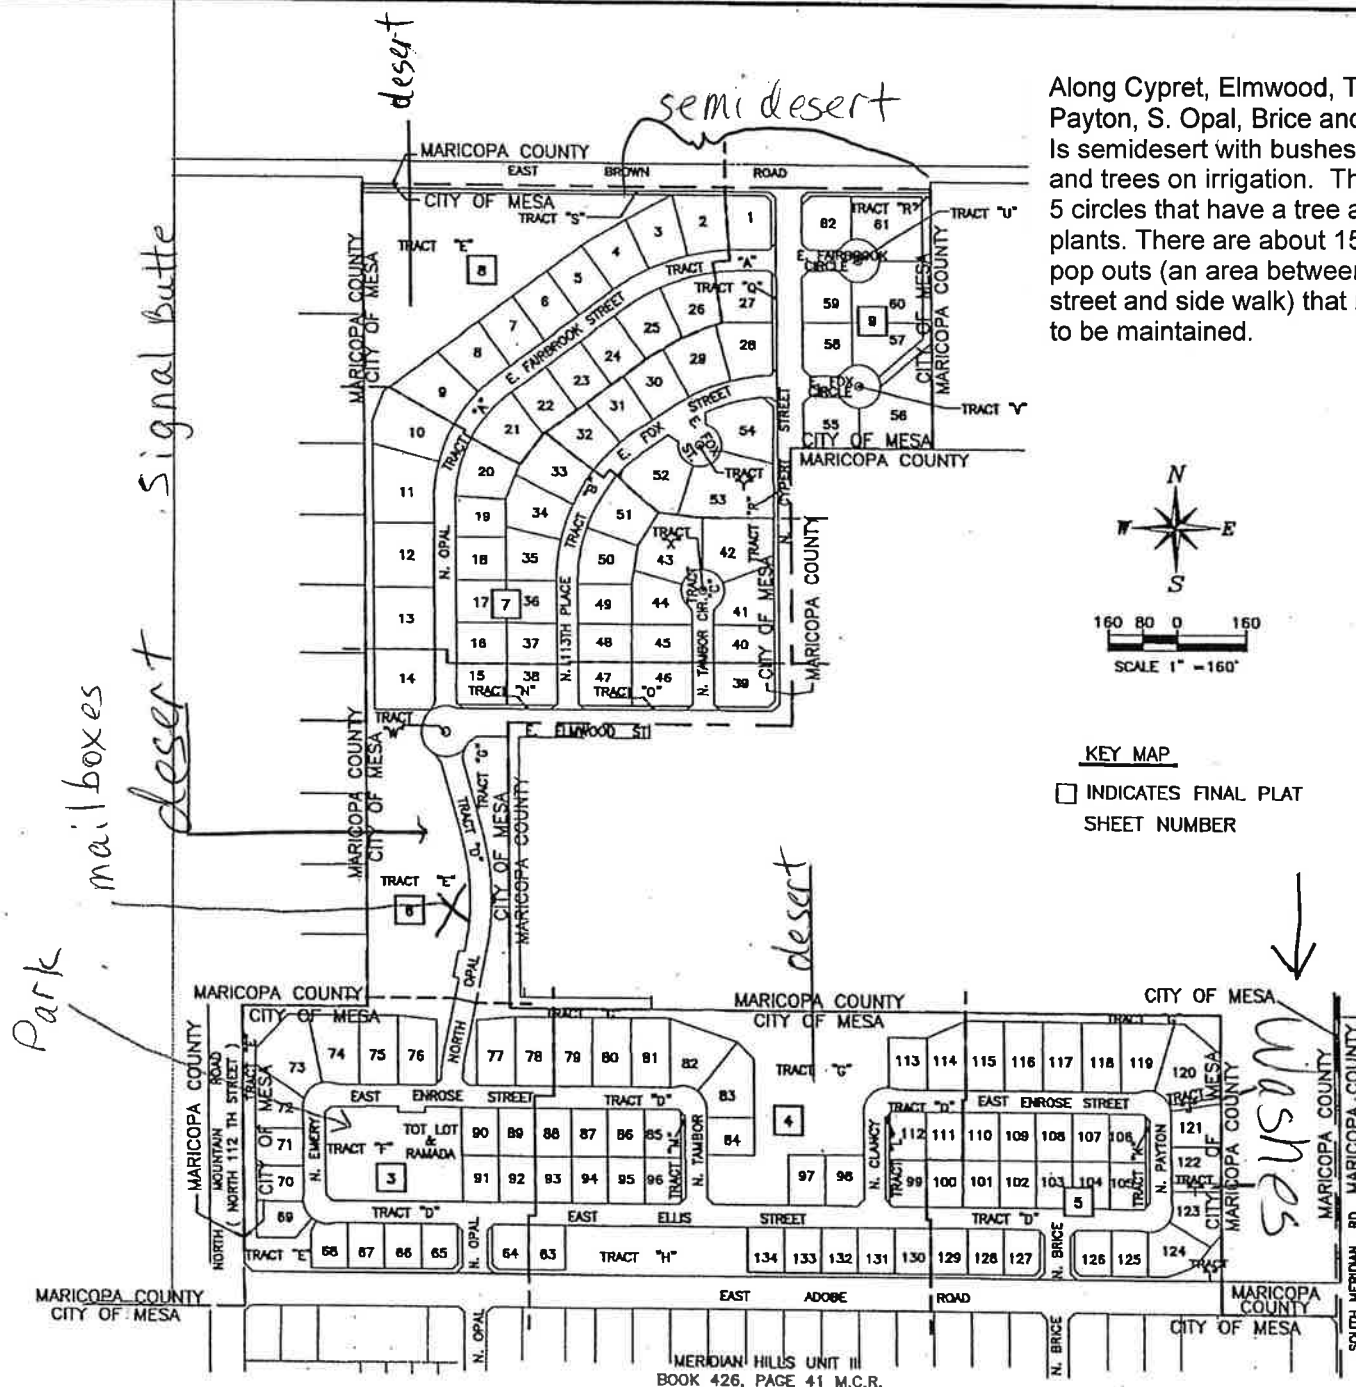

LOT AREAS		
LOT	AREA	
1	12,765 SQ. FT.	0.2936 ACRES
2	14,591 SQ. FT.	0.3327 ACRES
3	14,591 SQ. FT.	0.3327 ACRES
4	13,402 SQ. FT.	0.3077 ACRES
5	12,601 SQ. FT.	0.2893 ACRES
6	12,500 SQ. FT.	0.2875 ACRES
7	12,500 SQ. FT.	0.2875 ACRES
8	13,603 SQ. FT.	0.3123 ACRES
9	17,030 SQ. FT.	0.3909 ACRES
10	20,201 SQ. FT.	0.4615 ACRES
11	23,728 SQ. FT.	0.5437 ACRES
12	21,000 SQ. FT.	0.4821 ACRES
13	21,000 SQ. FT.	0.4821 ACRES
14	20,504 SQ. FT.	0.4759 ACRES
15	11,838 SQ. FT.	0.2719 ACRES
16	11,833 SQ. FT.	0.2716 ACRES
17	11,833 SQ. FT.	0.2716 ACRES
18	11,833 SQ. FT.	0.2716 ACRES
19	10,213 SQ. FT.	0.2327 ACRES
20	14,222 SQ. FT.	0.3255 ACRES
21	15,052 SQ. FT.	0.3453 ACRES
22	12,798 SQ. FT.	0.2923 ACRES
23	12,500 SQ. FT.	0.2875 ACRES
24	12,290 SQ. FT.	0.2803 ACRES
25	13,934 SQ. FT.	0.3199 ACRES
26	14,147 SQ. FT.	0.3248 ACRES
27	14,216 SQ. FT.	0.3277 ACRES
28	14,174 SQ. FT.	0.3253 ACRES
29	15,434 SQ. FT.	0.3543 ACRES
30	13,098 SQ. FT.	0.3007 ACRES
31	12,073 SQ. FT.	0.2772 ACRES
32	13,485 SQ. FT.	0.3086 ACRES
33	15,228 SQ. FT.	0.3507 ACRES
34	15,373 SQ. FT.	0.3529 ACRES
35	13,379 SQ. FT.	0.3117 ACRES
36	11,841 SQ. FT.	0.2720 ACRES
37	11,874 SQ. FT.	0.2721 ACRES
38	11,840 SQ. FT.	0.2721 ACRES
39	15,047 SQ. FT.	0.3454 ACRES
40	13,352 SQ. FT.	0.3065 ACRES
41	15,228 SQ. FT.	0.3507 ACRES
42	20,903 SQ. FT.	0.4799 ACRES
43	19,754 SQ. FT.	0.4532 ACRES
44	13,800 SQ. FT.	0.3155 ACRES
45	13,300 SQ. FT.	0.3052 ACRES
46	15,090 SQ. FT.	0.3455 ACRES
47	13,478 SQ. FT.	0.3084 ACRES
48	11,875 SQ. FT.	0.2726 ACRES
49	11,875 SQ. FT.	0.2726 ACRES
50	14,511 SQ. FT.	0.3331 ACRES
51	14,511 SQ. FT.	0.3331 ACRES
52	18,606 SQ. FT.	0.4271 ACRES
53	27,821 SQ. FT.	0.6387 ACRES
54	17,582 SQ. FT.	0.4038 ACRES
55	14,511 SQ. FT.	0.3331 ACRES
56	28,963 SQ. FT.	0.6658 ACRES
57	14,244 SQ. FT.	0.3270 ACRES
58	13,237 SQ. FT.	0.3043 ACRES
59	13,287 SQ. FT.	0.3049 ACRES
60	21,217 SQ. FT.	0.4871 ACRES
61	22,026 SQ. FT.	0.5056 ACRES
62	13,591 SQ. FT.	0.3120 ACRES
63	9,350 SQ. FT.	0.2148 ACRES
64	9,350 SQ. FT.	0.2148 ACRES
65	9,350 SQ. FT.	0.2148 ACRES
66	9,350 SQ. FT.	0.2148 ACRES
67	9,350 SQ. FT.	0.2148 ACRES


County Parcels

Salerno Ranch

23+

drawn
grid

typical maint @ 50% SIZED AND
culverts under Brown are CITY OF MESA

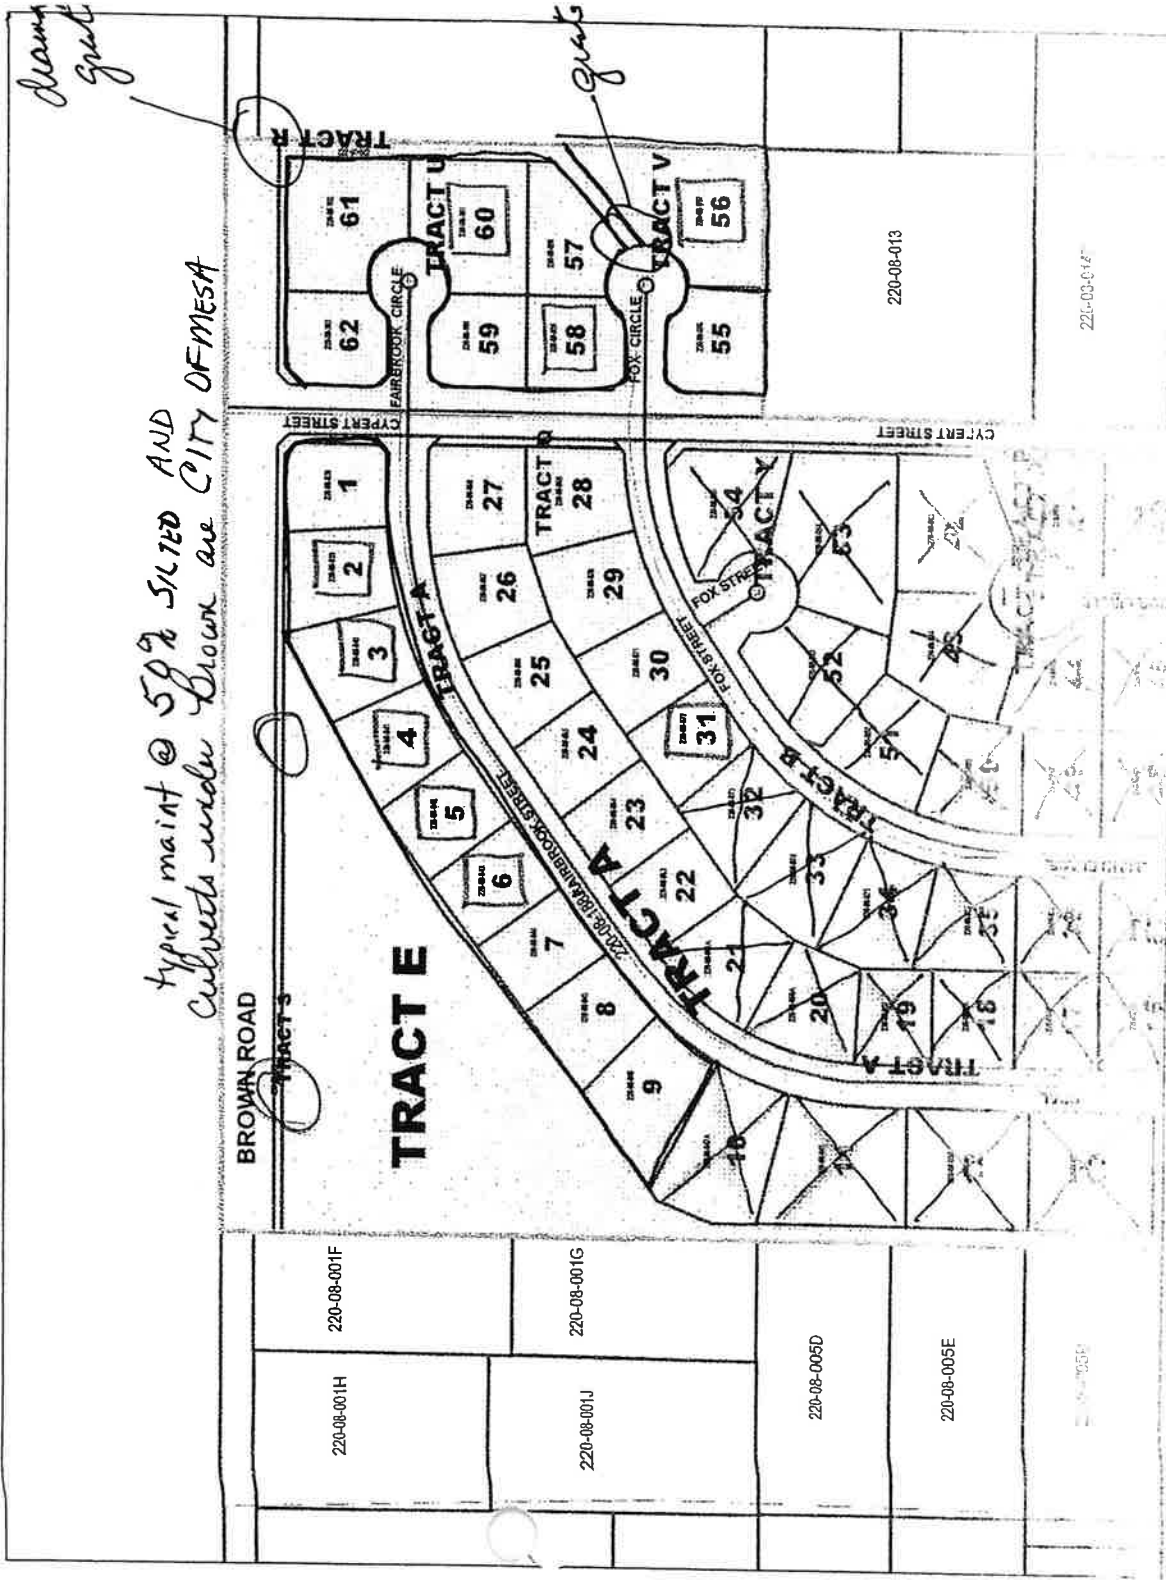

[illegible]

County Parcels

